Teil B - Textliche Festsetzungen

1. Das sonstige Sondergebiet gemäß § 11 BauNVO dient der Errichtung eines Technologiezentrums für Forschung, Lehre und Dienstleistung.
   Zulässig sind
   - Gebäude und Räume für Forschungs- und Hochschuleinrichtungen, für Büro-, Verwaltungs- und freiberufliche Nutzungen sowie für kulturelle, soziale, gesundheitliche und sportliche Zwecke,
   - Schank- und Speisewirtschaften
   - Einzelhandelsbetriebe mit max. 1.200 m² Geschossfläche und max. 799 m² Verkaufsfläche und folgenden Sortimenten:
     -- Nahrungsmittel, Getränke und Tabakwaren
     -- medizinische, orthopädische, kosmetische Artikel, einschließlich Drogerieartikel und pharmazeutische Artikel (Apotheken)
     -- Bücher, Zeitschriften, Zeitungen, Schreibwaren und Bürobedarf.

2. Im Baugebiet sind die überbaubaren Grundstücksflächen durch Baugrenzen bestimmt. Stellplätze und Garagen gemäß § 12 BauNVO, Nebenanlagen gemäß § 14 BauNVO sowie Zufahrten und Wege sind auch außerhalb der überbaubaren Grundstücksflächen zulässig.

3. Bei Abgang von Bäumen, für die der Bebauungsplan eine Erhaltungsbindung festsetzt, ist gleichartiger Ersatz (mit einem Stammumfang von mindestens 20 cm, gemessen in 1,0 m Höhe) zu pflanzen.

4. Entlang der westlichen Zufahrt (Planstraße A) sind insgesamt 16 Bäume mit einem Stammumfang von mindestens 16-18 cm zu pflanzen. Es wird die Verwendung von Arten der Pflanzenliste 1 empfohlen.

5. Beim Bauteil (BT) 02a sind mindestens 15 %, beim Bauteil (BT) 02c mindestens 40 % der Dachflächen zu begrünen. Für die Begrünung ist eine Sedum-Kräuter- oder Gräsermischung zu verwenden.

6. Zum Schutz vor Verkehrslärm müssen bei Errichtung, Änderung oder Nutzungsänderung baulicher Anlagen die Außenbauteile schutzbedürftiger Aufenthaltsräume der Gebäude im Sondergebiet „Technologiezentrum für Forschung, Lehre und Dienstleistung", bewertete Gesamtbauschalldämm-Maße ($R'_{w,ges}$) aufweisen, die nach der Norm DIN 4109-1; 2018 Schallschutz im Hochbau - Teil 1: „Mindestanforderungen" und Teil 2: „Rechnerische Nachweise" zu berechnen sind mit der Gleichung
   $R'_{w,ges} = L_a - K_{Raumart}$
   mit L_a = maßgeblicher Außenlärmpegel
   mit $K_{Raumart}$ = 35 dB für Büroräume und ähnliche Räume
   Der Nachweis der Erfüllung dieser Anforderungen ist im Baugenehmigungsverfahren unter Anwendung der Regelungen der DIN 4109-2; 2018 Schallschutz im Hochbau - Teil 2: „Rechnerische Nachweise" zu erbringen. Dabei sind im Schallschutznachweis insbesondere die Korrektur der Verhältnisse Raum-Fassadenfläche zu Raum-Grundfläche sowie die nach DIN 4109 geforderten Sicherheitsbeiwerte zu beachten.
   Folgende maßgebliche Außenlärmpegel sind maximal an den einzelnen Bauteilen zu erwarten:
   BT01, maximal 73 dB(A) (Ostfassade)
   BT01, maximal 73 dB(A) (Nord- und Südfassade)
   BT01, maximal 71 dB(A) (Westfassade)
   BT02a, maximal 73 dB(A) (Nord-, Nordwest- Südostfassade)
   BT02c, maximal 72 dB(A) (Südostfassade)
   BT02c, maximal 71 dB(A) (Westfassade)
   BT02c, maximal 69 dB(A) (Nordfassade)

7. Für den Artenschutz sind folgende Maßgaben zu erfüllen:
   a) Die am Bestandsgebäude vorhandenen Nistkästen sind zu erhalten.
   b) Im Baugebiet sind zusätzliche Nistkästen für Vögel im folgenden Umfang vorzusehen:

Arten mit Brutstätten im UG	Anzahl BR im UG	Anzahl betroffener BR im UG	Nistkästen als Höhle	Halbhöhle
Bachstelze	1	1		2x 2HW
Blaumeise	1	1	2x Nisthöhle 2M/FT Ø 26 mm	
Kohlmeise	2	2	4x Nisthöhle 2M/FT Ø 32 mm	
Hausrotschwanz	2	2		4x 2HW
Feldsperling	2	2	4x 3-fach Sperlingskoloniekästen (Unterputz) 1SP	-
Haussperling	1	1	2x 3-fach Sperlingskoloniekästen (Unterputz) 1SP	-
Anzahl künstlicher Nisthilfen:		**12**		**6**

   c) Fledermauskästen sind im Baugebiet im folgenden Umfang vorzusehen:

Artenschutzrechtliche Maßnahme	Artengruppe/Art	Bezeichnung	Menge
Fledermausersatzquartiere	gebäudebewohnende Kleinfledermausarten Sommerquartiere selbstreinigend	Oberschale 3FE mit isolierter Rückwand	3 Stück
	gebäudebewohnende Kleinfledermausarten Winterquartiere selbstreinigend	Fledermaushöhle 2 WI (Unterputz, speziell für wetterexponierte Lagen)	3 Stück


   d) Bei der Gestaltung der Fassaden und Fenster sind geeignete Maßnahmen zur Vermeidung von Vogelschlag und zur Reduzierung des signifikanten Tötungsrisikos nach § 44 Abs. 1 Nr. 1 BNatSchG nach vorheriger Abstimmung mit der unteren Naturschutzbehörde auszuführen.

Pflanzlisten

Pflanzenliste 1: Laubbäume

Acer campestre	Feldahorn
Alnus spaethii	Purpur-Erle
Carpinus betulus	Hainbuche
Fraxinus excelsior	Esche
Koelreuteria paniculata	Blasenbaum
Quercus robur	Stieleiche
Tilia platyphyllos	Sommerlinde
Ulmus 'New Horizon'	Ulme

Teil A - Planzeichnung

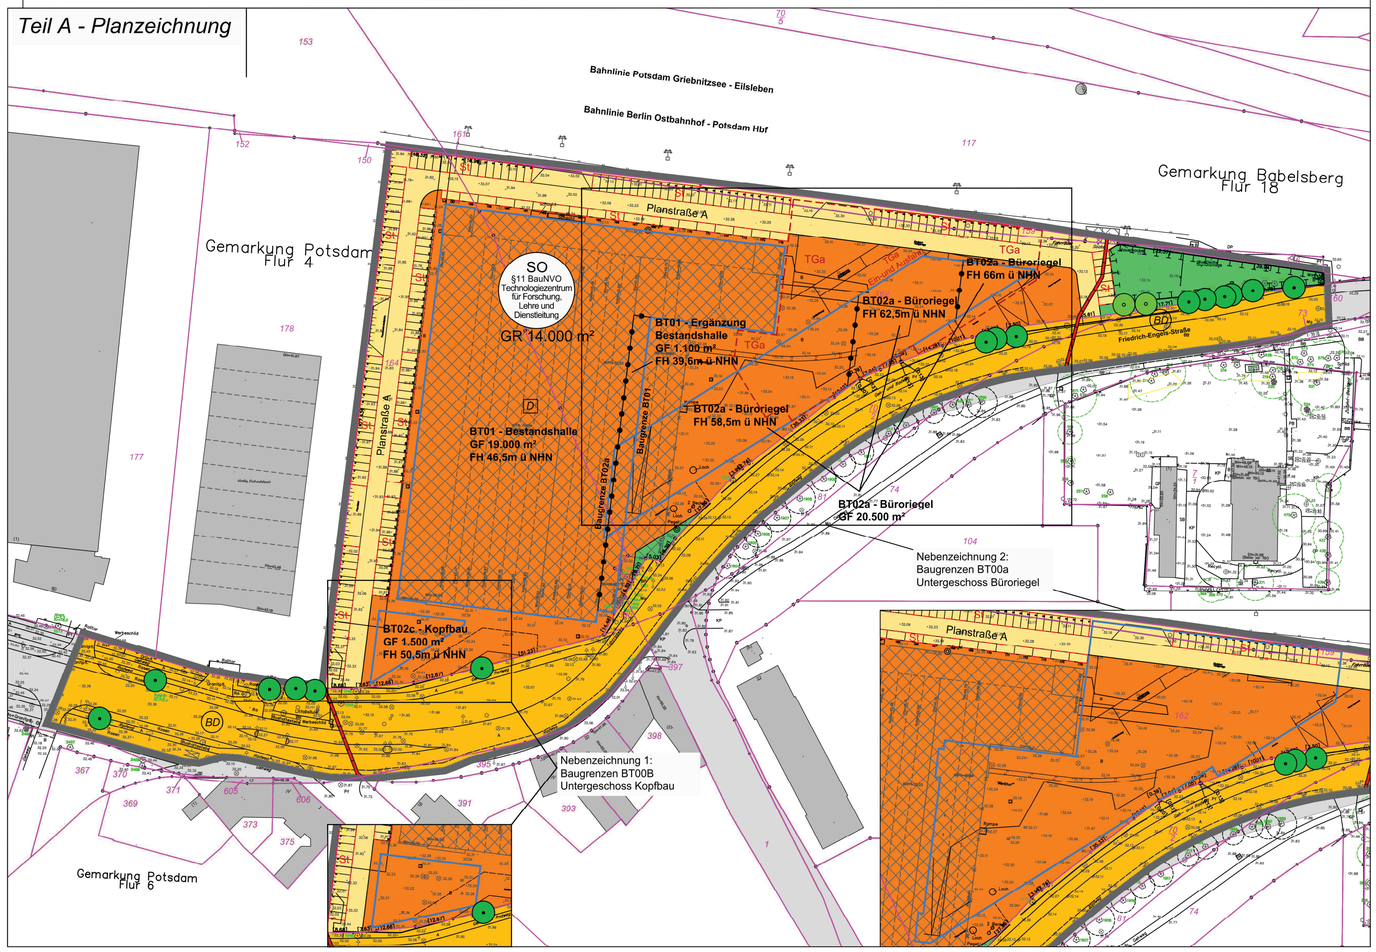

Landeshauptstadt Potsdam

Vorhabenbezogener Bebauungsplan Nr. 36

"Neue Halle / östliches RAW-Gelände"

Planzeichenerklärung

Art und Maß der baulichen Nutzung

- SO — Sonstiges Sondergebiet "Technologiezentrum für Forschung, Lehre und Dienstleistung"
- GR Grundfläche (als Höchstmaß)
  GF Geschossfläche (als Höchstmaß)
  FH Höhe baulicher Anlagen als Höchstmaß z.B. Firsthöhe über Normalhöhennull (NHN) im DHHN2016
- **Überbaubare Grundstücksfläche** — Baugrenze
- **Flächen für Stellplätze und Garagen** — TGa - Zweckbestimmung Tiefgarage; ST - Zweckbestimmung Stellplätze
- **Verkehrsflächen** — Öffentliche Straßenverkehrsflächen
- Private Verkehrsflächen
- Straßenbegrenzungslinie
- **private Grünflächen**

Planungen, Nutzungsregelungen, Maßnahmen und Flächen für Maßnahmen zum Schutz, zur Pflege und zur Entwicklung von Natur und Landschaft

- Umgrenzung von Flächen für Maßnahmen zum Schutz, zur Pflege und zur Entwicklung von Natur und Landschaft
- Anpflanzen von Bäumen, Sträuchern und sonstigen Bepflanzungen — Anpflanzen: Bäume
- Bindungen für Bepflanzungen und für die Erhaltung von Bäumen und Sträuchern und sonstigen Bepflanzungen sowie von Gewässern — Erhaltung: Bäume

Regelungen für die Stadterhaltung und für den Denkmalschutz


- (BD) — Umgrenzung von Gesamtanlagen (Ensembles), die dem Denkmalschutz unterliegen; BD - Bodendenkmal
- D — Einzelanlagen, die dem Denkmalschutz unterliegen

Sonstige Planzeichen

- Grenze des räumlichen Geltungsbereiches des Bebauungsplans
- Abgrenzung unterschiedlicher Nutzungen

Sonstige Darstellungen ohne Normcharakter

- 70 — Flurstücksgrenze
- Flurstücksnummer
- 10,00 / 32,18 — Vermaßungen örtlich gemessene Höhe in m ü. NHN im DHHN2016
- Gebäudebestand

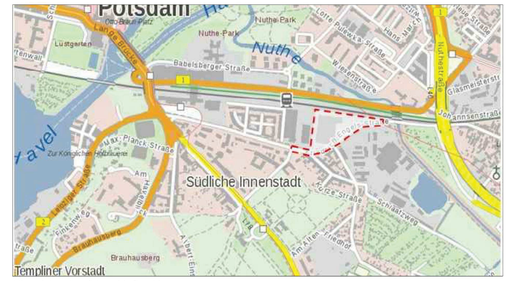

Übersichtsplan (ohne Maßstab)
zum Vorhabenbezogenen Bebauungsplan Nr. 36 "Neue Halle / östliches RAW-Gelände"

Hinweise ohne Normcharakter

Altlasten

Im Plangebiet im Bereich der Flur 4 mit den Flurstücken 159,162 und 164 ist ein teilsanierter Altstandort mit der Registriernummer 0305540451 und der Bezeichnung *Teilgebiet des ehemaligen Reichsausbesserungswerkes Potsdam (RAW) „Neue Halle"* im Altlasten- / Altlastenverdachtsflächenkataster der Landeshauptstadt Potsdam geführt.

Die Boden- und Grundwasserverunreinigung innerhalb der denkmalgeschützten Halle wurde teilsaniert, aber nicht völlig beseitigt. Bei Umbau- oder Rückbaumaßnahmen von Gebäudeteilen ist mit weiteren Untersuchungen und Auflagen zu rechnen.

Artenschutz

Vor Durchführung von Baumaßnahmen und vor Beseitigung von Vegetationsbeständen ist zu prüfen, ob die artenschutzrechtlichen Verbotsvorschriften des § 44 Abs. 1 BNatSchG für besonders geschützte Tierarten (z.B. Vögel, Fledermäuse) gemäß § 7 Abs. 2 Nr. 13 b und Nr. 14 c BNatSchG eingehalten werden. Andernfalls sind bei der jeweils zuständigen Behörde artenschutzrechtliche Ausnahmegenehmigungen (§ 45 Abs. 7 BNatSchG) einzuholen. Hieraus können sich besondere Beschränkungen/ Auflagen für die Baumaßnahmen ergeben (z.B. Regelung der Bauzeiten, Herstellung von Ersatzquartieren).

Nachrichtliche Übernahmen

Baudenkmale

Im Geltungsbereich des Bebauungsplanes befindet sich das Baudenkmal „Neue Halle". Die Regelungen des Brandenburger Denkmalschutzgesetzes sind zu beachten.

Bodendenkmale

Der Planbereich berührt zwei Bodendenkmale i.S.v. § 2 Abs. 1,2 Nr. 4 i.V.m. § 3 Abs. 1 BbgDSchG. Die Realisierung von Bodeneingriffen (z.B. Tiefbaumaßnahmen) ist erst nach Abschluss archäologischer Dokumentations- und Bergungsmaßnahmen in organisatorischer und finanzieller Verantwortung der Bauherren (§ 9 Abs. 3 und 4 BbgDSchG) und Freigabe durch die Denkmalschutzbehörde zulässig. Die Bodeneingriffe sind erlaubnispflichtig (§ 9 Abs. 1 BbgDSchG).

Hinweis: Zu diesem Bebauungsplan gehört ein entsprechender Vorhaben- und Erschließungsplan

Rechtsgrundlagen

- Baugesetzbuch (BauGB) in der Fassung der Bekanntmachung vom 3. November 2017 (BGBl. I S. 3634)
- Baunutzungsverordnung (BauNVO) in der Fassung der Bekanntmachung vom 21. November 2017 (BGBl. IS. 3786)
- Brandenburgische Bauordnung (BbgBO) vom 19. Mai 2016 (GVBl. I/16, [Nr. 14]), zuletzt geändert durch Artikel 13 des Gesetztes vom 15. Oktober (GVBl.I/18, [Nr. 22], S. 28)
- Verordnung über die Ausarbeitung der Bauleitpläne und die Darstellung des Planinhalts (PlanZV) vom 18.12.1990, zuletzt geändert durch Artikel 3 des Gesetzes vom 04.05.2017 (BGBl. I S. 1057)

Maßstab 1:1.000 i.O.

0 — 40 — 80 Meter

NORD

Plangrundlage:
Bestandsvermessung der öbVI Malon&Cuda, Alt Novawes 87, 14482 Potsdam
Maßstab: 1:1000 i.O.
Stand: Februar/März 2018 sowie Juli 2018 (Ergänzung Aufnahme Straße)
Höhensystem: DHHN2016
Lagesystem: ETRS89

August 2019
Entwurf

Landeshauptstadt Potsdam
Fachbereich Stadtplanung und Stadterneuerung
Bereich Verbindliche Bauleitplanung

Stand: 2019-08-26